


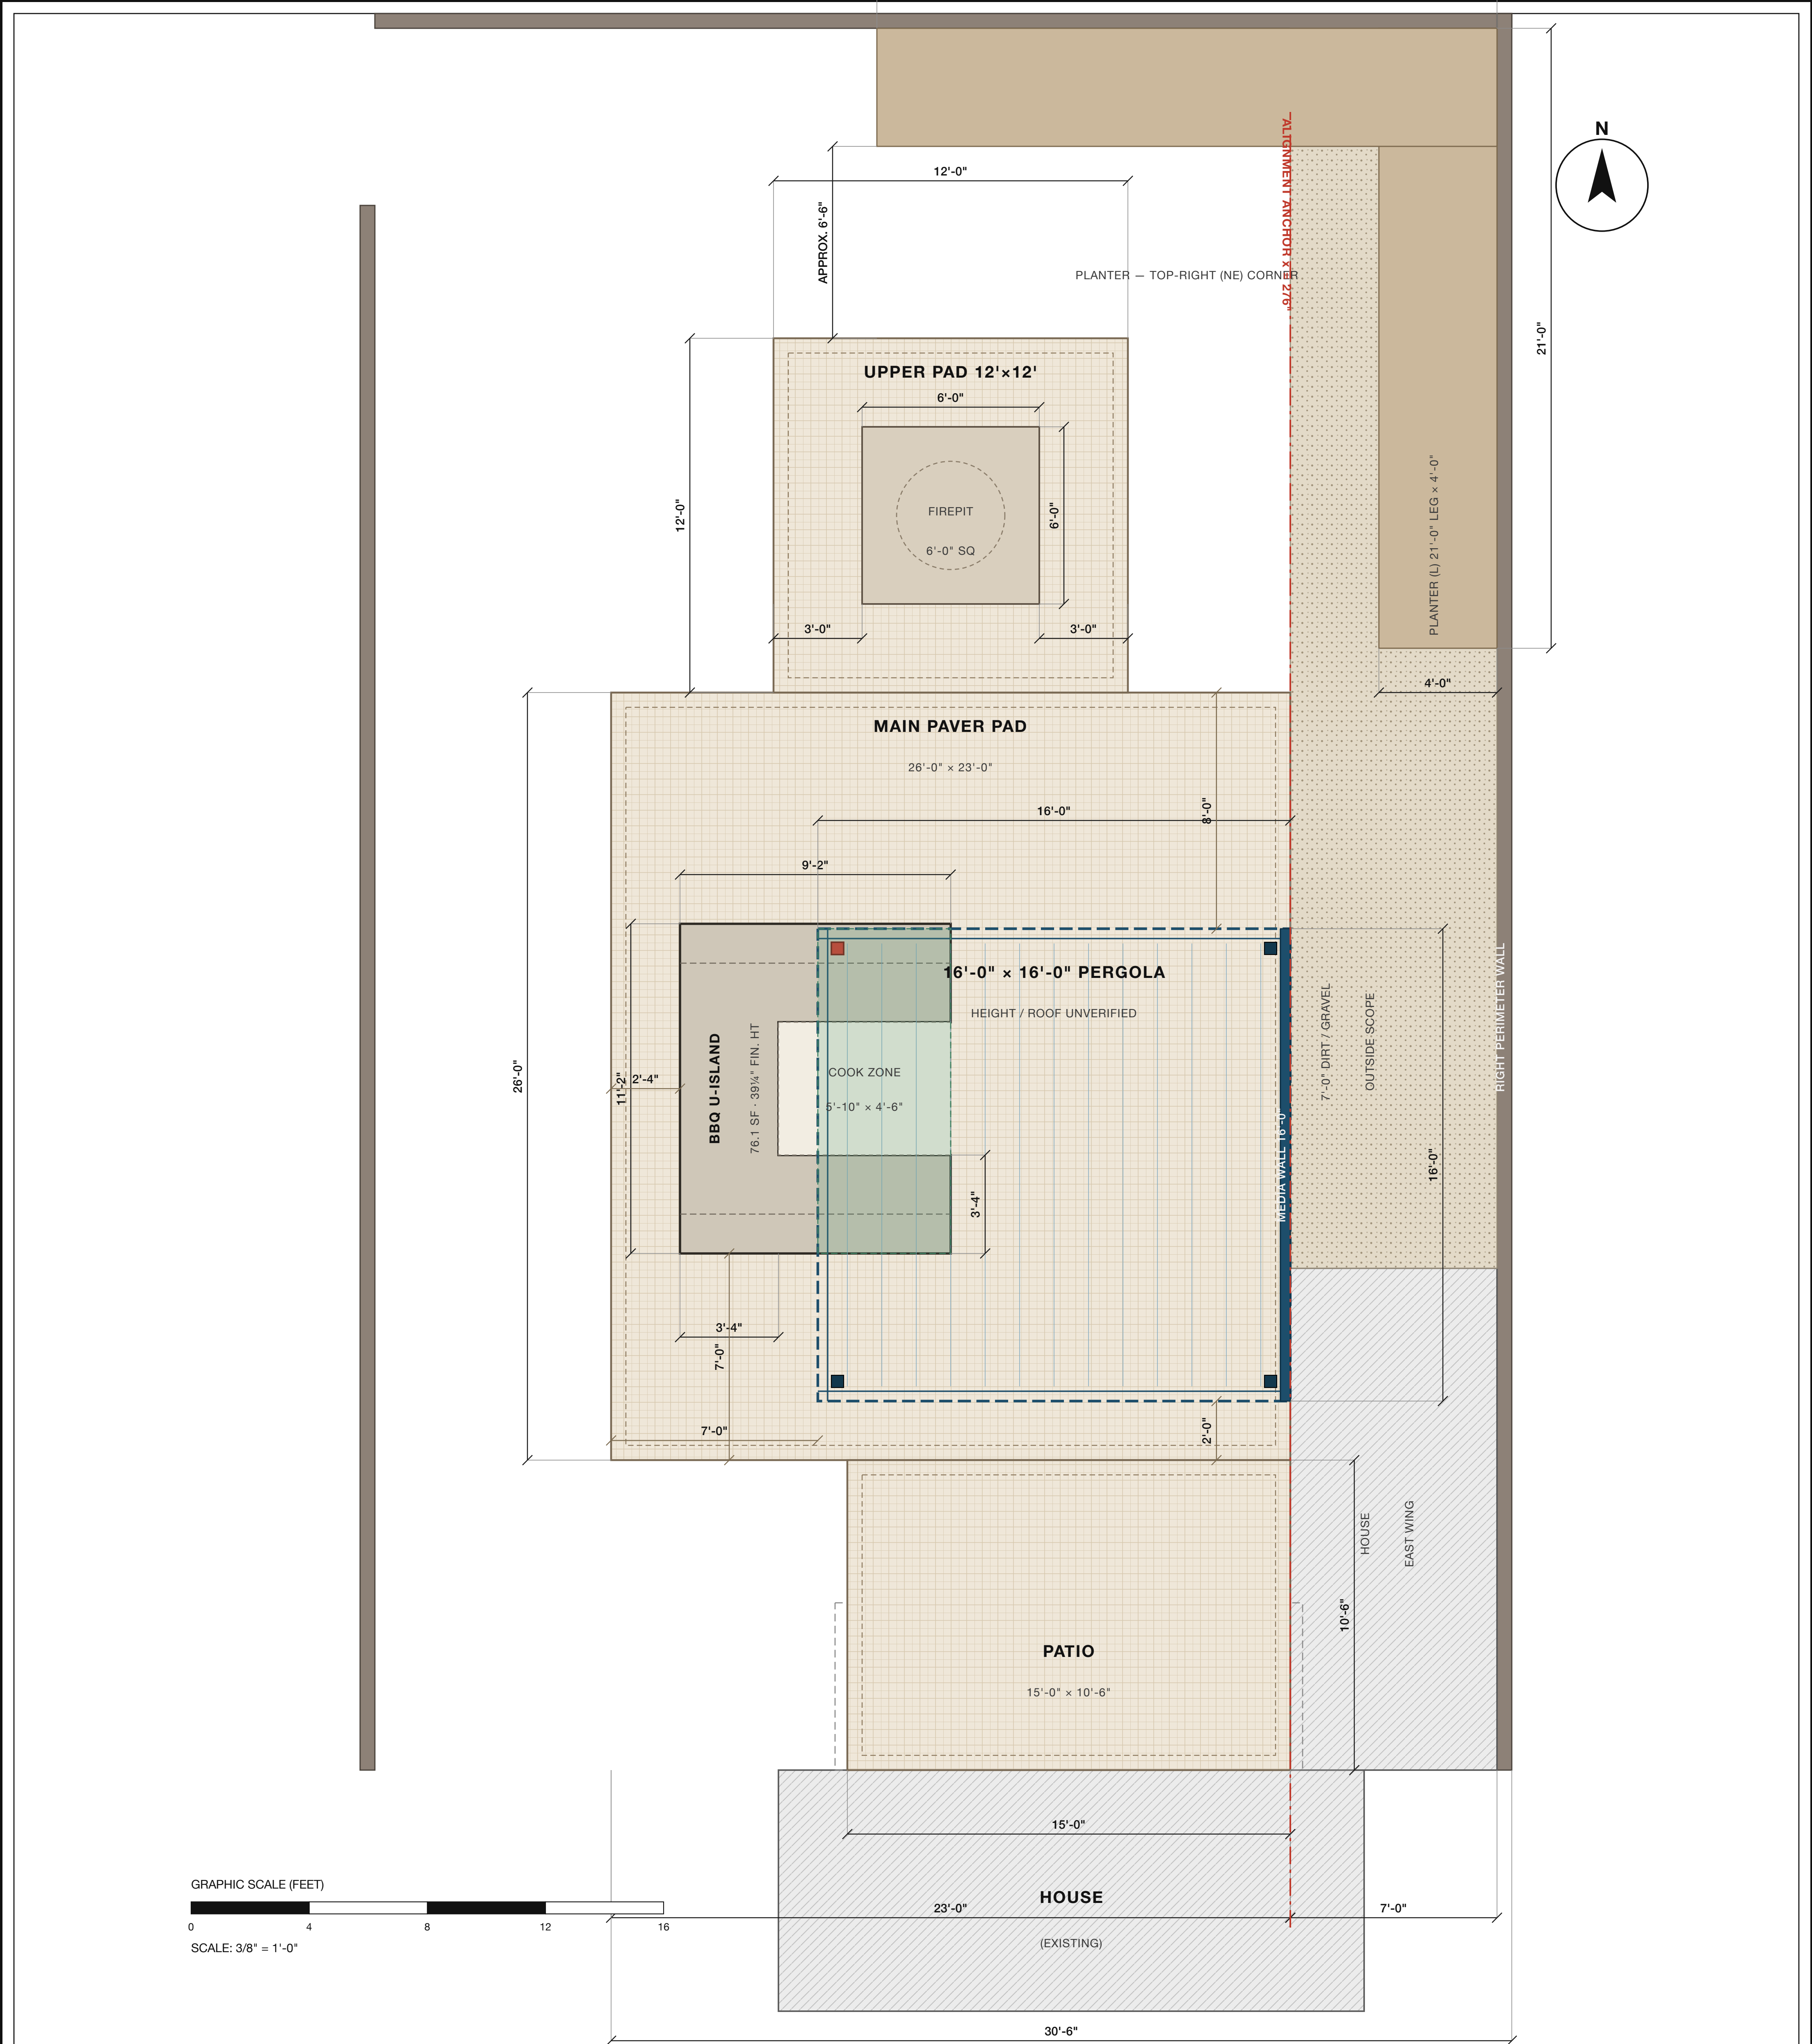

LEGEND	
	Proposed paver pad (main / patio / upper)
	6" paver soldier border
	BBQ U-island, masonry counter
	Open cook zone (inside U)
	Pergola outline, 16'-0" sq
	Media wall on aligned right edge
	Pergola post 5"×5"
	Cook zone sheltered by pergola roof
	7'-0" dirt / gravel - OUTSIDE SCOPE
	Perimeter wall (existing)
	House / structure (existing)
	Planter, 36" high
	Firepit footprint 6'-0" sq

GENERAL NOTES	
1. All dimensions in feet-inches. Datum 0,0 = SW corner of main paver pad.	
2. Dimensions taken from the locked registry in app/BackyardViewer.tsx. Verified against that source before export - see VERIFICATION panel.	
3. ALIGNMENT ANCHOR: the patio right edge and the main pad right edge share one continuous straight line at x = 276". The pergola media wall runs this same line. All right-side dimensions originate from it.	
4. The 7'-0" dirt/gravel strip and the right perimeter wall are OUTSIDE the paver/patio scope. Shown for context only. No hardscape in that strip.	
5. The pergola INTENTIONALLY overlaps and shelters the BBQ. The overlap is by design, not a conflict: 49.5 sq ft of cook zone falls under roof.	
6. Pergola support posts are oriented toward the BBQ side (west pair).	
6a. PLANTER is shown at the TOP-RIGHT (NE) corner. Both outer-face legs remain 21'-0". The north leg is shown approximately 6'-8" beyond the upper pad. Placement is provisional and must be verified in the field.	
7. LOCKED: pads, borders, firepit footprint, BBQ dimensions, pergola plan size, right-edge alignment, 7'-0" margin, pergola placement.	
8. UNVERIFIED: pergola height and roof build-up; firepit construction; BBQ and planter placement; house massing and walls are photo-derived.	
⚠️ CONSTRUCTABILITY ISSUE FOUND DURING VERIFICATION	
Pergola post at x=92", z=208" lands ON the BBQ counter. A 5"×5" post cannot bear on the 40"-wide masonry counter run. The roof is meant to shelter the BBQ, but a POST inside its footprint is not buildable. FIX A - shift the pergola 13" north (z 24 → 37). Post clears the counter at z 218; pergola north edge moves to 229, still inside the pad (312). Nothing else changes: the media wall stays on the anchor and shelter area is kept.	

VERIFICATION — CHECKED vs LOCKED GEOMETRY						
	ACTUAL	EXP		ACTUAL	EXP	
main pad width	276	276	OK	bbq footprint sf	76.11	76.1 OK
main pad depth	312	312	OK	pergola width	192	192 OK
patio width	180	180	OK	pergola depth	192	192 OK
patio depth	126	126	OK	media wall == depth	192	192 OK
upper pad width	144	144	OK	pergola E edge on anchor	276	276 OK
upper pad depth	144	144	OK	pergola within pad (N)	0	0 OK
firepit width	72	72	OK	upper pad centered on main pad	138	138 OK
firepit depth	72	72	OK	firepit ctr in upper (x)	138	138 OK
patio R edge == pad R edge	276	276	OK	firepit ctr in upper (z)	384	384 OK
anchor == 276	276	276	OK	planter east leg depth	48	48 OK
margin starts at anchor	276	276	OK	planter east leg run	252	252 OK
margin width 7'-0"	84	84	OK	planter north leg depth	48	48 OK
wall at margin end	360	360	OK	planter north leg run	252	252 OK
wall thickness	6	6	OK	planter abuts right wall	360	360 OK
bbq cook width	54	54	OK	planter abuts north wall	582	582 OK
bbq cook depth	70	70	OK	planter legs share NE cnr	360	360 OK
bbq overhang	16	16	OK	planter clear of pad	0	0 OK
bbq counter run	274	274	OK	planter gap from upper pad	78	78 OK
36 checks run · 36 passed · 0 failed · BBQ footprint 76.1 sf						

SONORAN HORIZON LLC		IRVIN RESIDENCE	
Landscape · Hardscape · Outdoor Living		BACKYARD RENOVATION	
2D DIMENSIONED SITE PLAN		SHEET A-1.0	
SCALE	3/8" = 1'-0"	DATE	2026-08-03
SHEET SIZE	24" × 36" (ARCH D)	REV	04 — turf removed; planter gap shown
UNITS	Feet-inches (model: inches)	DRAWN	Generated from locked geometry
DATUM	0,0 = SW corner, main pad	STATUS	NOT FOR CONSTRUCTION