


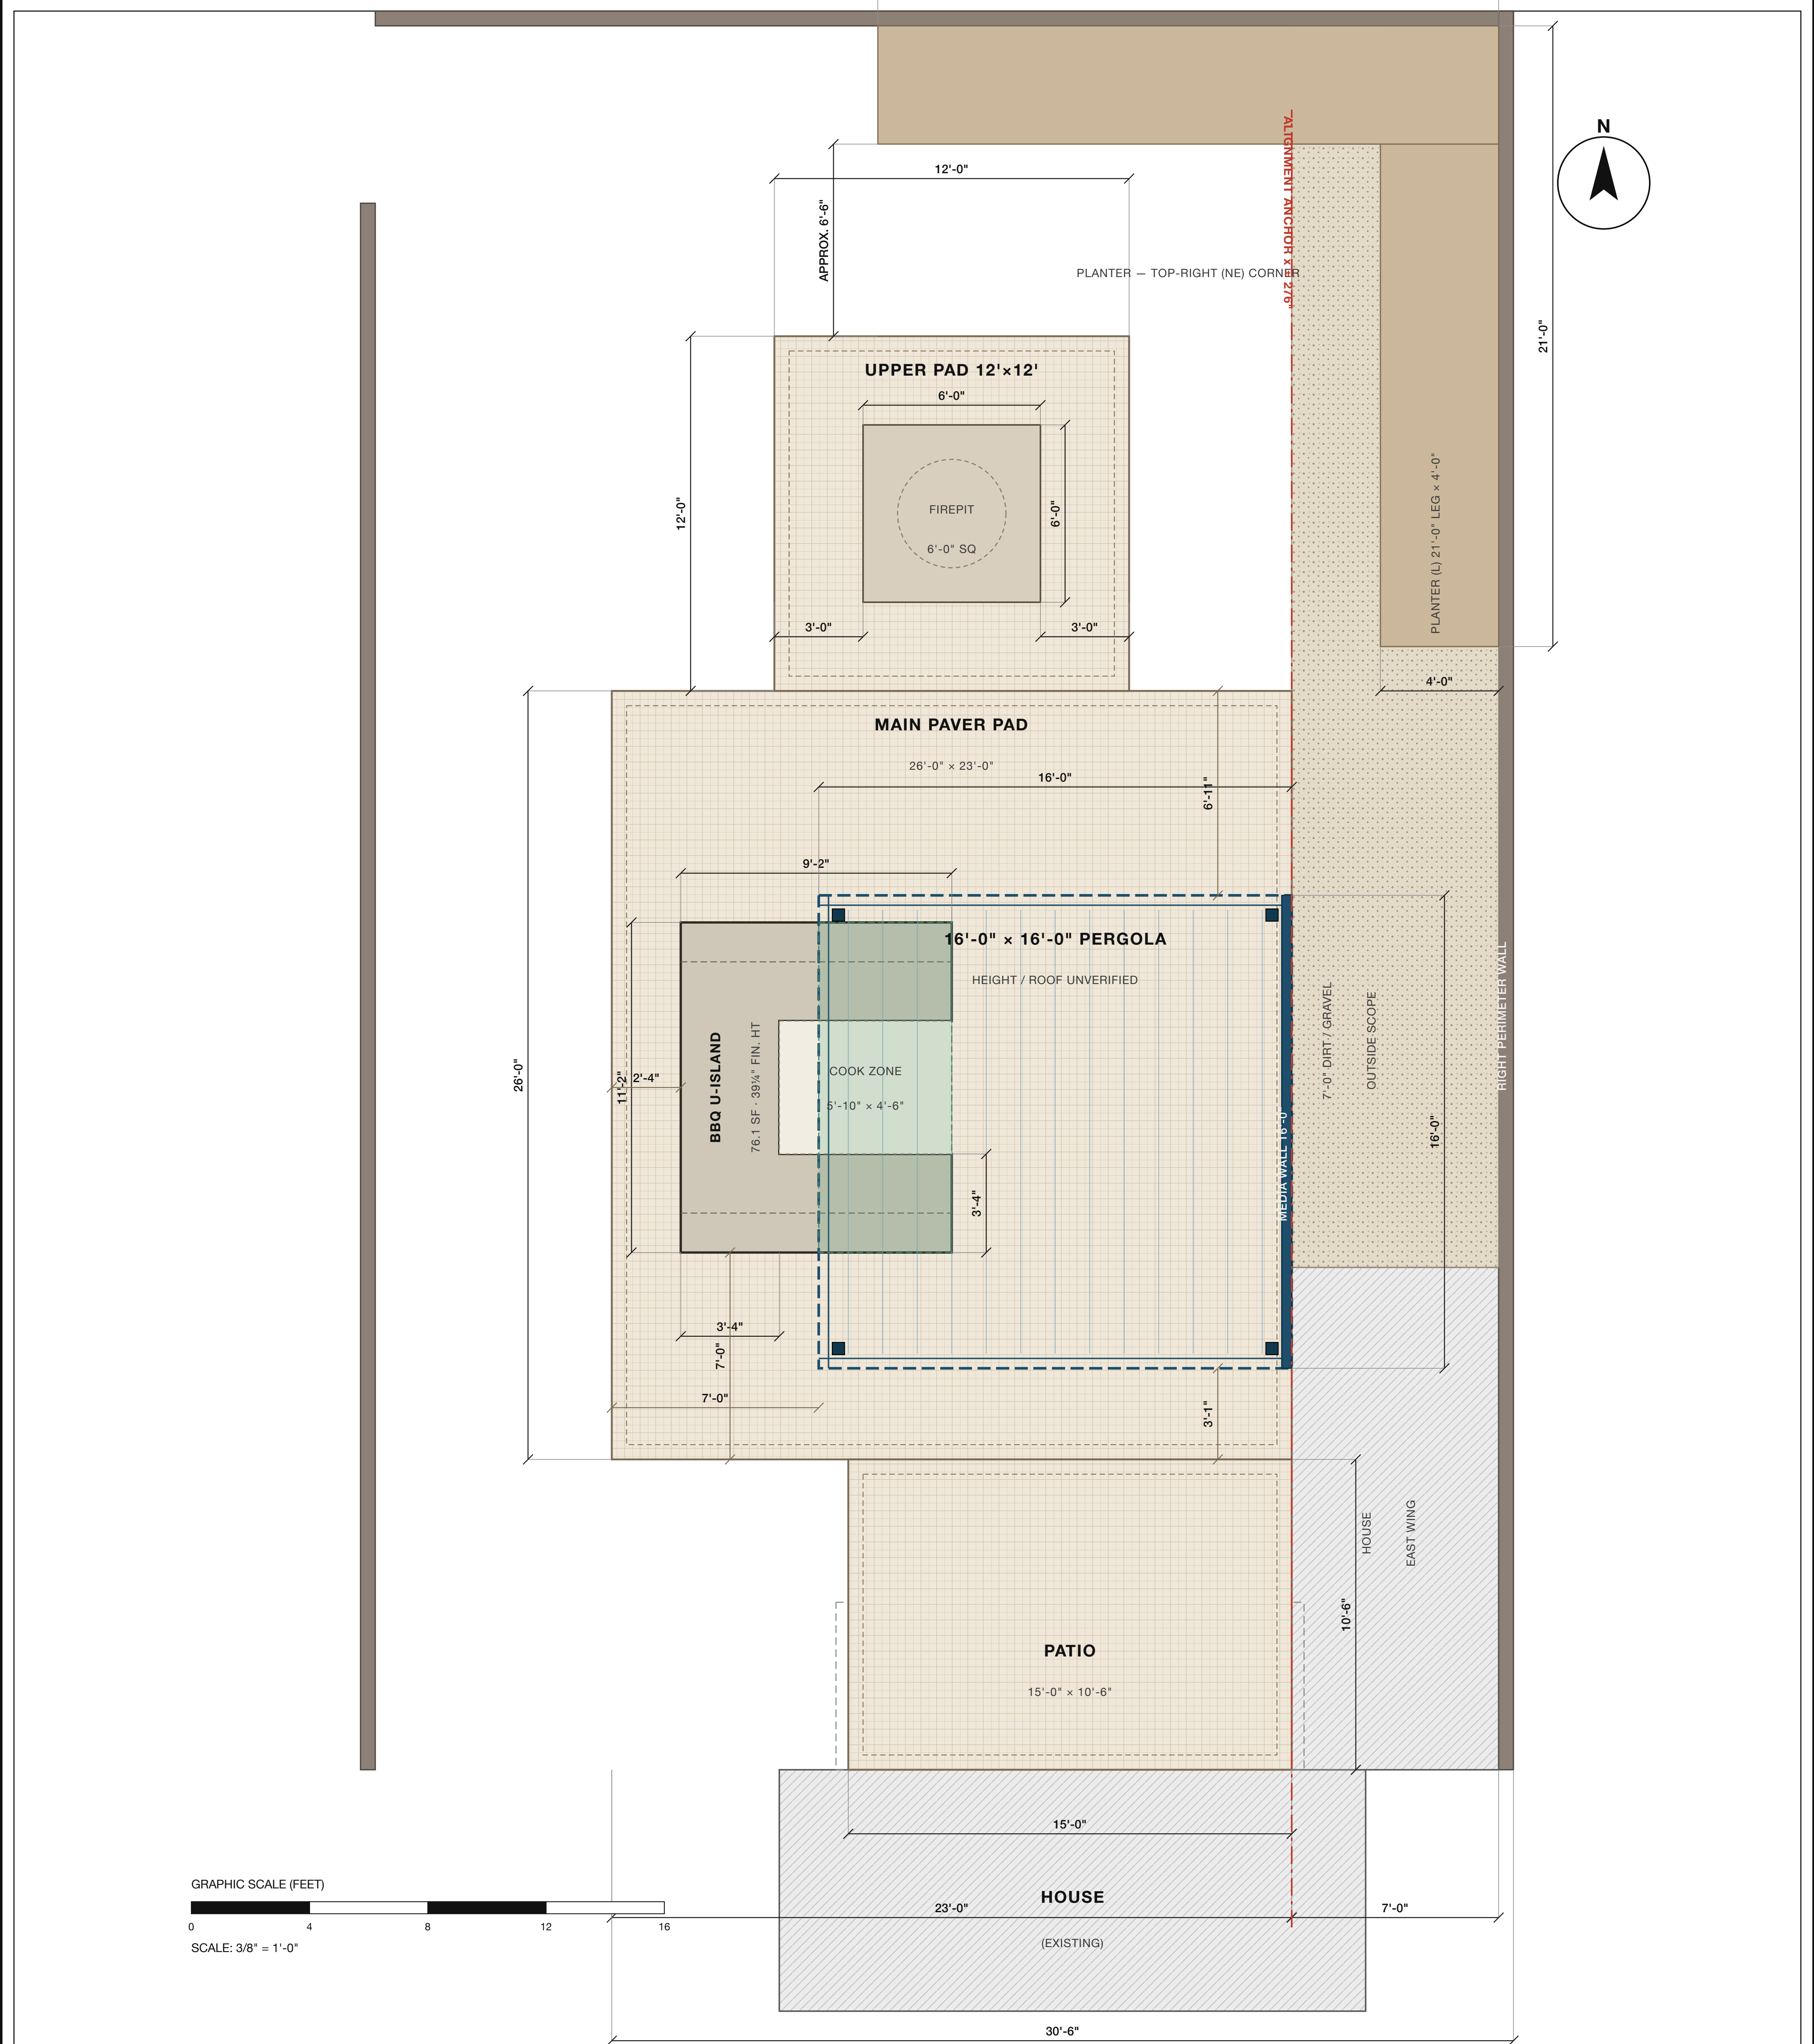

LEGEND	
	Proposed paver pad (main / patio / upper)
	6" paver soldier border
	BBQ U-island, masonry counter
	Open cook zone (inside U)
	Pergola outline, 16'-0" sq
	Media wall on aligned right edge
	Pergola post 5"x5"
	Cook zone sheltered by pergola roof
	7'-0" dirt / gravel - OUTSIDE SCOPE
	Perimeter wall (existing)
	House / structure (existing)
	Planter, 36" high
	Firepit footprint 6'-0" sq

GENERAL NOTES	
1. All dimensions in feet-inches. Datum 0,0 = SW corner of main paver pad.	
2. Dimensions taken from the locked registry in app/BackyardViewer.tsx. Verified against that source before export - see VERIFICATION panel.	
3. ALIGNMENT ANCHOR: the patio right edge and the main pad right edge share one continuous straight line at x = 276". The pergola media wall runs this same line. All right-side dimensions originate from it.	
4. The 7'-0" dirt/gravel strip and the right perimeter wall are OUTSIDE the paver/patio scope. Shown for context only. No hardscape in that strip.	
5. The pergola INTENTIONALLY overlaps and shelters the BBQ. The overlap is by design, not a conflict; 50.2 sq ft of cook zone falls under roof.	
6. OPTIMAL PERGOLA SELECTED: shifted 13" north from the sketch reference. Right/media-wall alignment is retained and all posts clear the BBQ counter.	
6a. PLANTER is shown at the TOP-RIGHT (NE) corner. Both outer-face legs remain 21'-0". The north leg is shown approximately 6'-6" beyond the upper pad. Placement is provisional and must be verified in the field.	
7. LOCKED: pads, borders, firepit footprint, BBQ dimensions, pergola plan size, right-edge alignment, 7'-0" margin, optimal pergola placement.	
8. UNVERIFIED: pergola height and roof build-up; firepit construction;	
PERGOLA CLEARANCE — OPTIMAL POSITION VERIFIED	
SELECTED: pergola shifted 13" north from the sketch reference (z 24 → 37). All four 5"x5" posts clear the BBQ masonry counter footprint. The right edge and integrated media wall remain on the x = 276" anchor. The 16'-0" x 16'-0" roof remains inside the main pad and shelters the cook zone. Pergola height and roof build-up remain unverified pending product selection.	

VERIFICATION — CHECKED vs LOCKED GEOMETRY						
	ACTUAL	EXP		ACTUAL	EXP	
main pad width	276	276	OK	bbq footprint sf	76.11	76.1 OK
main pad depth	312	312	OK	pergola width	192	192 OK
patio width	180	180	OK	pergola depth	192	192 OK
patio depth	126	126	OK	media wall == depth	192	192 OK
upper pad width	144	144	OK	pergola E edge on anchor	276	276 OK
upper pad depth	144	144	OK	pergola within pad (N)	0	0 OK
firepit width	72	72	OK	upper pad centered on main pad	138	138 OK
firepit depth	72	72	OK	firepit ctr in upper (x)	138	138 OK
patio R edge == pad R edge	276	276	OK	firepit ctr in upper (z)	384	384 OK
anchor == 276	276	276	OK	planter east leg depth	48	48 OK
margin starts at anchor	276	276	OK	planter north leg run	252	252 OK
margin width 7'-0"	84	84	OK	planter north leg depth	48	48 OK
wall at margin end	360	360	OK	planter north leg wall	252	252 OK
wall thickness	6	6	OK	planter abuts right wall	360	360 OK
bbq cook width	54	54	OK	planter abuts north wall	582	582 OK
bbq cook depth	70	70	OK	planter legs share NE cnr	360	360 OK
bbq overhang	16	16	OK	planter clear of pad	0	0 OK
bbq counter run	274	274	OK	planter gap from upper pad	78	78 OK
36 checks run · 36 passed · 0 failed · BBQ footprint 76.1 sf						

BACKYARD RENOVATION PLAN		DIMENSIONED CONCEPT PLAN	
Unbranded client review sheet		CLIENT REVIEW	
2D DIMENSIONED SITE PLAN		SHEET A-1.0	
SCALE	3/8" = 1'-0"	DATE	2026-08-03
SHEET SIZE	24" x 36" (ARCH D)	REV	06 — unbranded; optimal pergola selected
UNITS	Feet-inches (model: inches)	DRAWN	Generated from locked geometry
DATUM	0,0 = SW corner, main pad	STATUS	NOT FOR CONSTRUCTION